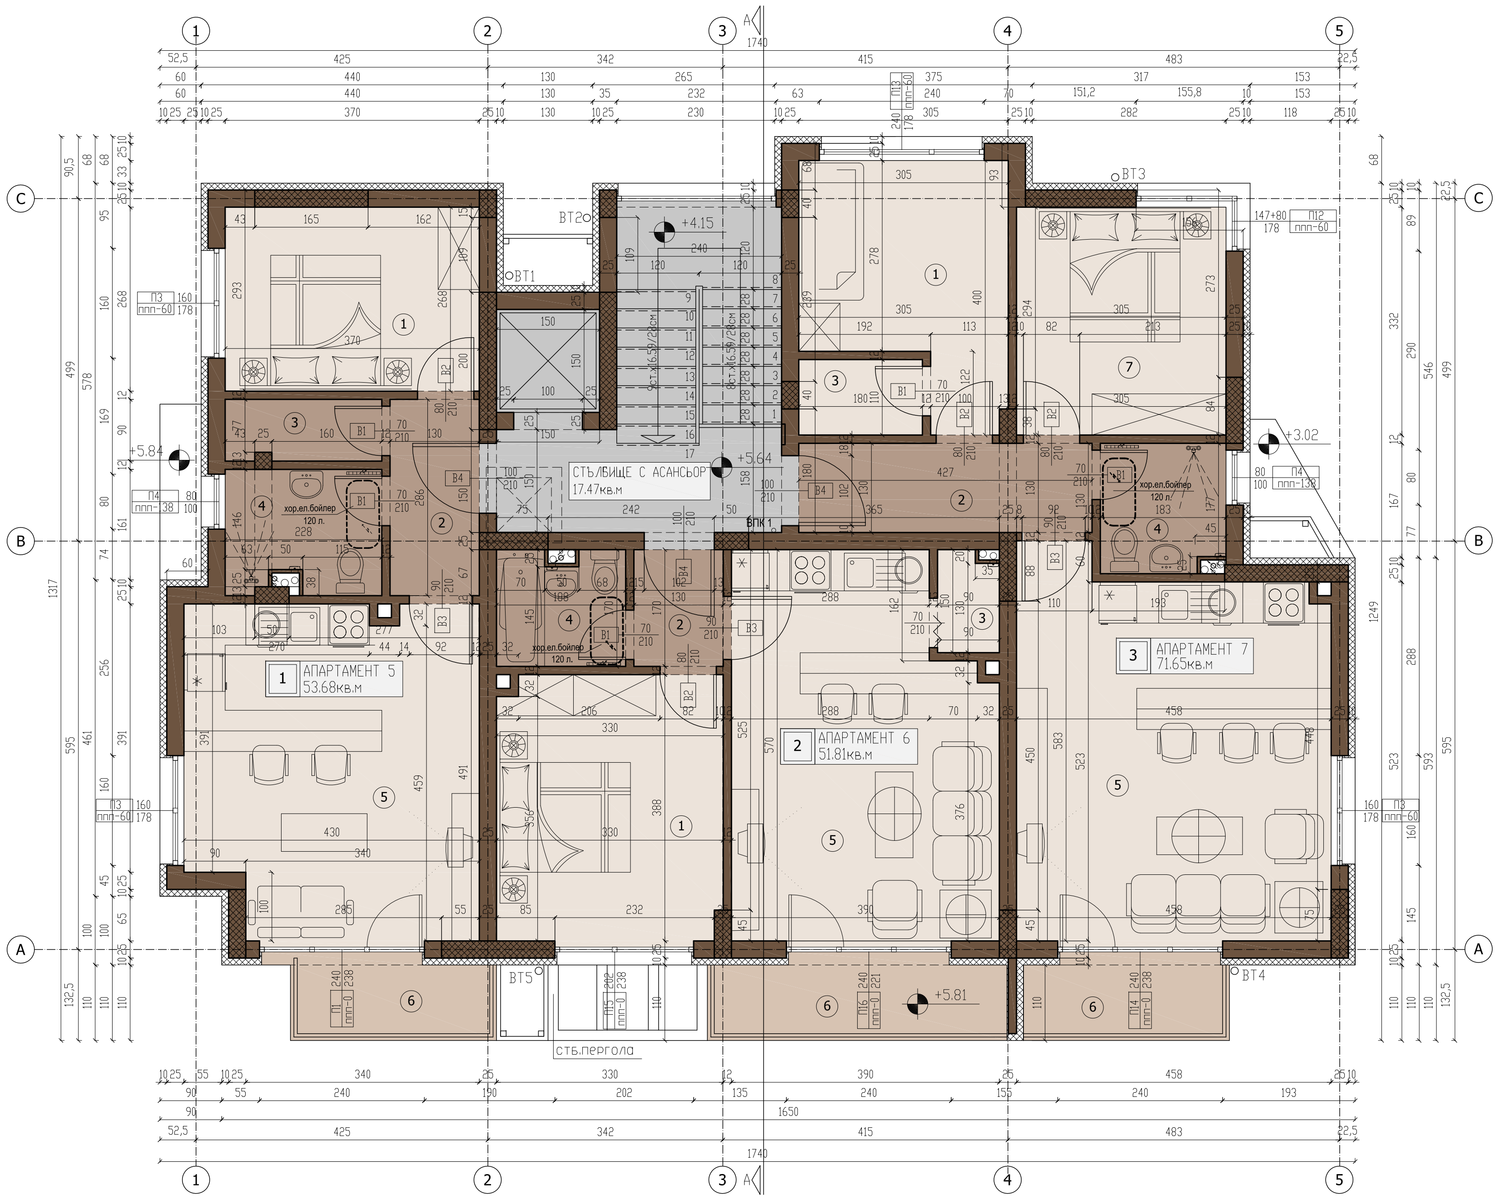

ИЗОЛАЦИИ И НАСТИЛКИ

А. ПОКРИВ-ПЛОСЪК

- 2 пласта битумна хидроизолация
- армирана цим.замазка -4см
- топлоизолация - XPS 12см с коефициент на топлопроводност 0,030W/mK
- пароизолация
- стб.плоча 18см
- грунд
- гипсова мазилка -8мм
- финна шпакловка гипсова по тавани върху мазилка, вкл. шлайфане
- латекс-едноцветно по тавани-грунд с две покривки ръце боя

Б. ВЪНШНИ СТЕНИ

- Силикат модифицирана мазилка, притисната
- грунд
- шпакловка
- стъклофибърна мрежа
- EPS -25 до 30кг/м3- 10см с коефициент на топлопроводност 0,035W/mK, с клас по реакция на огън Е
- лепило
- дълбокопроникващ грунд
- тухлена зидария 25см
- грунд
- гипсова мазилка -8мм
- финна шпакловка гипсова по стени върху мазилка, вкл. шлайфане
- латекс-едноцветно по стени-грунд с две покривки ръце боя

Г. ТЕРАСА НАД ОТОПЛЯЕМО ПОМЕЩЕНИЕ

- гранитогрес клас 1 с COF коефициент по-голям от 0,7
- високо еластично, хидро и мразоустойчиво лепило за тънкослойно полагане
- мазана двукомпонентна хидроизолация
- изравнителна циментова замазка с наклон -от 2см до 6см
- полиетиленово фолио
- топлоизолация-XPS 12см
- пароизолационен слои от битумна мембрана
- стб.плоча-18см
- гипсова мазилка -8мм
- финна шпакловка гипсова по тавани върху мазилка, вклшлайфане
- латекс-едноцветно по таван-грунд с две покривки ръце боя

Д. ОБРЪЩАНЕ НА ТОПЛОИЗОЛАЦИЯ ОКОЛО ОТВОРИ

- Силикат модифицирана мазилка, притисната
- грунд
- шпакловка
- стъклофибърна мрежа
- XPS - 2см с коефициент на топлопроводност 0,030W/mK
- лепило
- дълбокопроникващ грунд
- тухлена зидария 25см

АПАРТАМЕНТ 5 - 53.68 кв.м.

1	СПАЛНЯ	9.92кв.м	ЛАМПАРКЕТ	ЛАТЕКС	ЛАТЕКС
2	ПРЕДВЕРИЕ С КОРИДОР	4.10кв.м	ТЕРАКОТА	ЛАТЕКС	ЛАТЕКС
3	СКЛАД	2.02кв.м	ТЕРАКОТА	ЛАТЕКС	ЛАТЕКС
4	БАНЯ С WC	3.71кв.м	ТЕРАКОТА	ФАЯНС	ЛАТЕКС
5	ДНЕВНА С КУХН. БОКС	20.29кв.м	ЛАМПАРКЕТ	ЛАТЕКС	ЛАТЕКС
6	БАЛКОН	3.74кв.м	СТУДОУСТ. ГРАНИТОГРЕС		

АПАРТАМЕНТ 6 - 51.81 кв.м.

1	СПАЛНЯ	12.82кв.м	ЛАМПАРКЕТ	ЛАТЕКС	ЛАТЕКС
2	ПРЕДВЕРИЕ С КОРИДОР	2.51кв.м	ТЕРАКОТА	ЛАТЕКС	ЛАТЕКС
3	СКЛАД	1.22кв.м	ЛАМПАРКЕТ	ЛАТЕКС	ЛАТЕКС
4	БАНЯ С WC	3.05кв.м	ТЕРАКОТА	ФАЯНС	ЛАТЕКС
5	ДНЕВНА С КУХН. БОКС	20.78кв.м	ЛАМПАРКЕТ	ЛАТЕКС	ЛАТЕКС
6	БАЛКОН	5.24кв.м	СТУДОУСТ. ГРАНИТОГРЕС		

АПАРТАМЕНТ 7 - 71.65 кв.м.

1	СПАЛНЯ	9.89кв.м	ЛАМПАРКЕТ	ЛАТЕКС	ЛАТЕКС
2	ПРЕДВЕРИЕ С КОРИДОР	5.94кв.м	ТЕРАКОТА	ЛАТЕКС	ЛАТЕКС
3	СКЛАД	1.98кв.м	ЛАМПАРКЕТ	ЛАТЕКС	ЛАТЕКС
4	БАНЯ С WC	3.29кв.м	ТЕРАКОТА	ФАЯНС	ЛАТЕКС
5	ДНЕВНА С КУХН. БОКС	24.73кв.м	ЛАМПАРКЕТ	ЛАТЕКС	ЛАТЕКС
6	БАЛКОН	3.30кв.м	СТУДОУСТ. ГРАНИТОГРЕС		
7	СПАЛНЯ	10.13кв.м	ЛАМПАРКЕТ	ЛАТЕКС	ЛАТЕКС
	СТЪЛБИЩЕ	17.47кв.м	ГРАНИТОГРЕС	ЛАТЕКС	ЛАТЕКС

ЗАБЕЛЕЖКИ:

1. РАЗМЕРИТЕ ПО КОТИРОВЪЧНИТЕ ЛИНИИ СА ЗИДАРСКИ, В САНТИМЕТРИ.
2. ОТВОРИТЕ НА ДОГРАМИТЕ СА ЗИДАРСКИ. ДА СЕ ВЗЕМАТ ДОПЪЛНИТЕЛНО МЕРКИ ОТ МЯСТО ЗА ИЗПЪЛНЕНИЕ НА ДОГРАМАТА.
3. ВСИЧКИ ПАРАПЕТИ ДА СЕ ИЗПЪЛНЯТ С ВИСОЧИНА 105 (СМ) ОТ ГОТОВ ПОД.
4. ПОДПРОЗОРЕЧНИТЕ ПАРАПЕТИ (ППП) СЕ МЕРЯТ ОТ КОТА ГОТОВ ПОД.
5. ТОПЛОИЗОЛАЦИЯТА ДА СЕ ИЗПЪЛНИ ОТВЪН НА ОГРАДНИТЕ ЕЛЕМЕНТИ.
6. ВИСОЧИНИТЕ НА ВРАТИТЕ СА ОТ КОТА ГОТОВ ПОД
7. ВСИЧКИ ИЗОЛАЦИОННИ РАБОТИ ДА СЕ ИЗПЪЛНЯВАТ ПО ТЕХНИЧЕСКО ПРЕДПИСАНИЕ ОТ ПРОИЗВОДИТЕЛЯ.
8. ВСИЧКИ ЦВЕТОВЕ И МАТЕРИАЛИ, НЕУКАЗАНИ В ЧЕРТЕЖА, СЛЕДВА ДА СЕ ИЗПЪЛНЯТ ПО ДОПЪЛНИТЕЛНО ПРЕДПИСАНИ УКАЗАНИЯ ОТ ПРОЕКТАНТА.
9. ВСИЧКИ КОМИНИ ДА СЕ ИЗЗИДАТ С ОГНЕОПОРНИ ТУХЛИ С КЛАС ПО РЕАКЦИЯ НА ОГЪН А2, С ОГНЕУСТОЙЧИВОСТ G 100. ФУГИТЕ ДА СЕ ЗАПЪЛНЯТ ПО ЦЯЛАТА ВИСОЧИНА.

ОБЩА ПЛОЩ НА НИВОТО-197.71кв.м, в това число 20.63кв.м общи части

ВЪЗЛОЖИТЕЛ: "БИЛДИНГ ЕКСПРЕС КР" ЕООД

СЪГЛАСУВАЛ:

ОБЕКТ: ЖИЛИЩНА СГРАДА И ИЗГРЕБНА ЯМА В УПИ X-268 (ПИ с идент.68134.1977.2642), КВ.31, м."ДРАГАЛЕВЦИ", РАЙОН "ВИТОША" - СО

ЧАСТ	ФАЗА	МАЩАБ	ЛИСТ NO.
АРХИТЕКТУРА	ТП	1:50	4

ОПИСАНИЕ НА ЧЕРТЕЖА: РАЗПРЕДЕЛЕНИЕ НА КОТА +5.64

ПЕЧАТ НА ПРОЕКТАНТА

Design:

СИА ЕСБ ЕООД
Тел: +359 87 850 74 04
WEB: www.siaesb.bg
E-mail: office@siaesb.bg

ПРОЕКТАНТИ			ПОДПИС
1.ПРОЕКТАНТ 2.СЪГЛАСУВАЩ	1	2	
АРХИТЕКТУРА: арх.Елена Ценова	■		
КОНСТРУКЦИИ: инж.Антон Милчев		■	
ЕЛЕКТРО ИНСТАЛАЦИИ: инж.Светлин Стайков		■	
ВиК: инж.Даниел Господинов		■	

ПРОЕКТАНТИ			ПОДПИС
1.ПРОЕКТАНТ 2.СЪГЛАСУВАЩ	1	2	
ОВК/ЕЕ: инж.Григор Зарков		■	
ПБ: инж.Слава Милчева		■	
ГЕОДЕЗИЯ И ВП: инж.Александър Милчев		■	
ПАРКОУСТРОЙСТВО: л.арх.Вероника Алексиева		■	

ПРОЕКТ N	РЕВИЗИЯ	ГОДИНА НА ИЗДАВАНЕ
	00	2018