


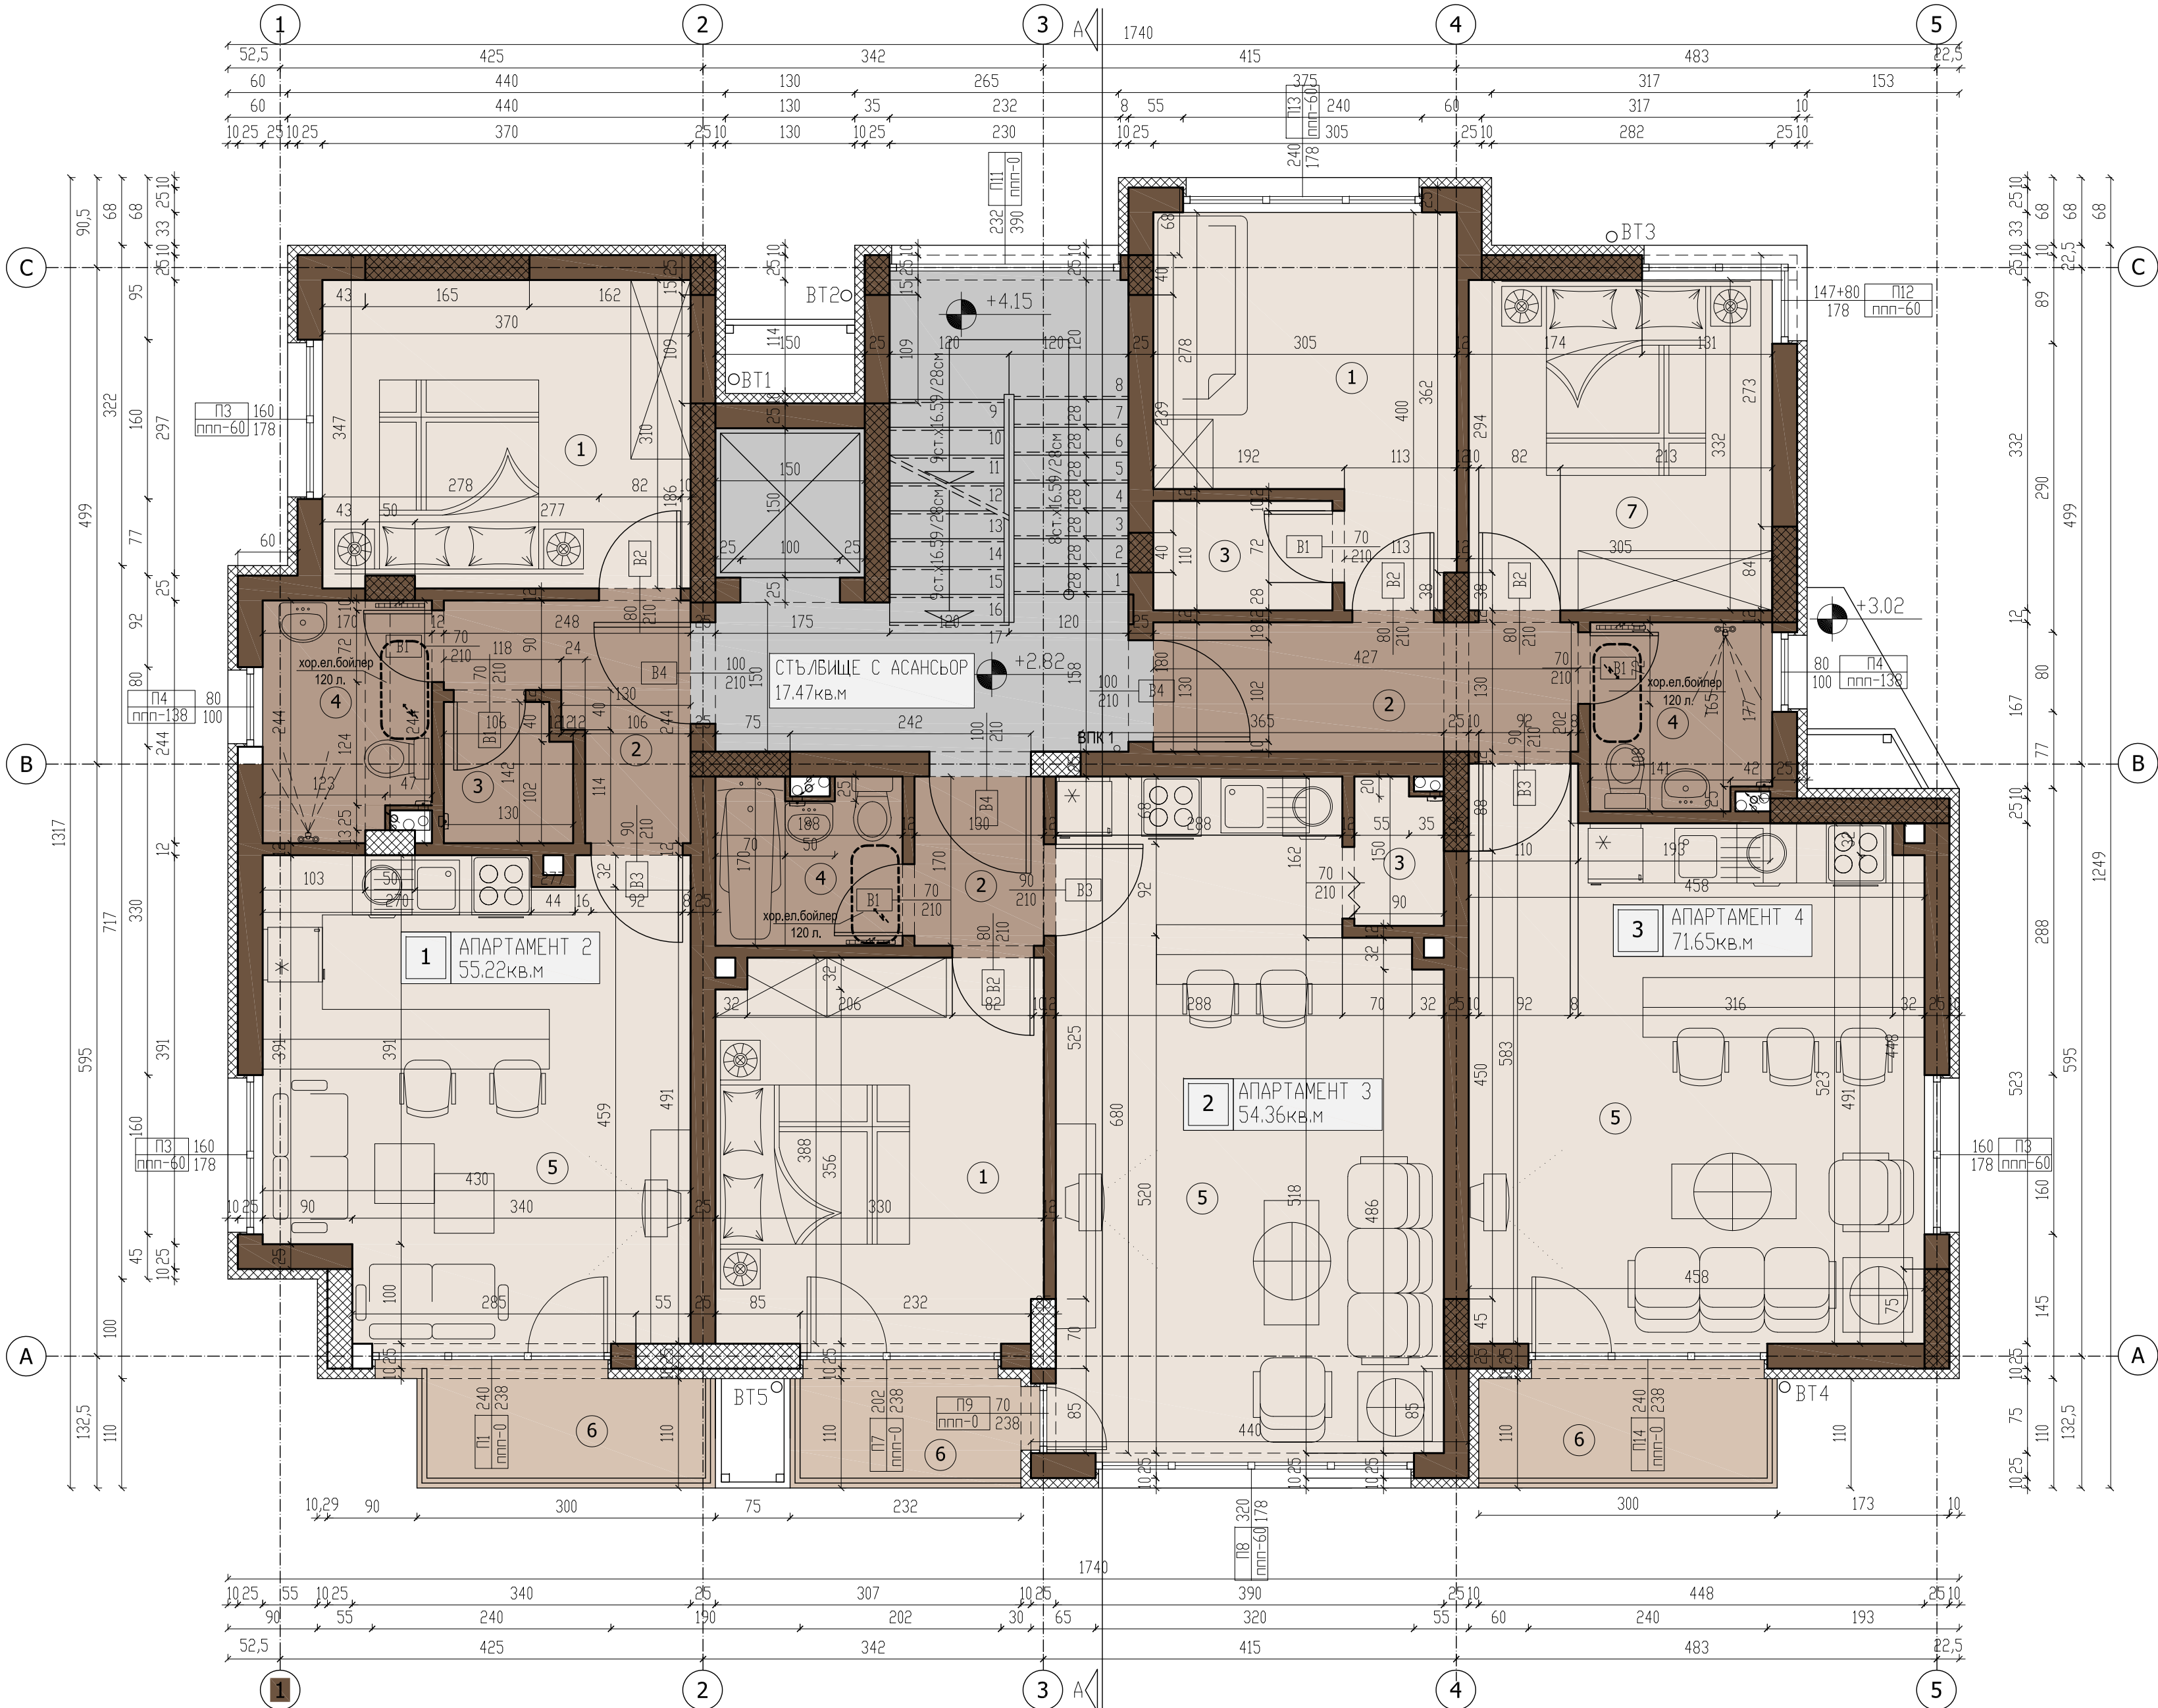

ИЗОЛАЦИИ И НАСТИЛКИ				
А. ПОКРИВ-ПЛОСЪК				
- 2 пласта битумна хидроизолация				
- армирана цим.замазка -4см				
- топлоизолация - XPS 12см с коефициент на топлопроводност 0,030W/mK				
- пароиолация				
- стъ.плоча 18см				
- гргнд				
- гипсова мазилка -8мм				
- финна шпакловка гипсова по тавани върху мазилка, вкл. шлайфане				
- латекс-едноцветно по тавани-грнд с две покриващи ръце боя				
Б. ВЪНШНИ СТЕНИ				
- Силикат модифицирана мазилка, притисната				
- гргнд				
- шпакловка				
- стъклофибърна мрежа				
- EPS -25 до 30кг/м3- 10см с коефициент на топлопроводност 0,035W/mK,				
с клас по реакция на огън Е				
- лепило				
- дълбокопроникващ гргнд				
- тухлена зидария 25см				
- гргнд				
- гипсова мазилка -8мм				
- финна шпакловка гипсова по стени върху мазилка, вкл.шлайфане				
- латекс-едноцветно по стени-грнд с две покриващи ръце боя				
Г. ТЕРАСА НАД ОТОПЛЯЕМО ПОМЕЩЕНИЕ				
- гранитогрес клас 1 с COF коефициент по-голям от 0,7				
- високо еластично, хидро и мразоустойчиво				
лепило за тънкослойно полагане				
- мазана двукомпонентна хидроизолация				
- изравнителна циментова замазка с наклон -от 2см до 6см				
- полиетиленово фолио				
- топлоизолация-XPS 12см				
- пароиолационен слой от битумна мембрана				
- стъ.плоча-18см				
- гипсова мазилка -8мм				
- финна шпакловка гипсова по тавани върху мазилка, вкл.шлайфане				
- латекс-едноцветно по таван-грнд с две покриващи ръце боя				
Д. ОБРЪЩАНЕ НА ТОПЛОИЗОЛАЦИЯ ОКОЛО ОТВОРИ				
- Силикат модифицирана мазилка, притисната				
- гргнд				
- шпакловка				
- стъклофибърна мрежа				
- XPS - 2см с коефициент на топлопроводност 0,030W/mK				
- лепило				
- дълбокопроникващ гргнд				
- тухлена зидария 25см				
АПАРТАМЕНТ 2 - 55.22 кв.м.				
1	СПАЛНЯ	11.4кв.м	ЛАМПАРКЕТ	ЛАТЕКС
2	ПРЕДВЕРИЕ С КОРИДОР	4.34кв.м	ТЕРАКОТА	ЛАТЕКС
3	СКЛАД	1.75кв.м	ТЕРАКОТА	ЛАТЕКС
4	БАНЯ С WC	3.90кв.м	ТЕРАКОТА	ФАЯНС
5	ДНЕВНА С КУХН. БОКС	20.29кв.м	ЛАМПАРКЕТ	ЛАТЕКС
6	БАЛКОН	3.74кв.м	СТУДОУСТ. ГРАНИТОГРЕС	
АПАРТАМЕНТ 3 - 54.36 кв.м.				
1	СПАЛНЯ	12.82кв.м	ЛАМПАРКЕТ	ЛАТЕКС
2	ПРЕДВЕРИЕ С КОРИДОР	2.51кв.м	ТЕРАКОТА	ЛАТЕКС
3	СКЛАД	1.24кв.м	ЛАМПАРКЕТ	ЛАТЕКС
4	БАНЯ С WC	3.05кв.м	ТЕРАКОТА	ФАЯНС
5	ДНЕВНА С КУХН. БОКС	25.20кв.м	ЛАМПАРКЕТ	ЛАТЕКС
6	БАЛКОН	2.55кв.м	СТУДОУСТ. ГРАНИТОГРЕС	
АПАРТАМЕНТ 4 - 71.65 кв.м.				
1	СПАЛНЯ	9.89кв.м	ЛАМПАРКЕТ	ЛАТЕКС
2	ПРЕДВЕРИЕ С КОРИДОР	5.94кв.м	ТЕРАКОТА	ЛАТЕКС
3	СКЛАД	1.98кв.м	ЛАМПАРКЕТ	ЛАТЕКС
4	БАНЯ С WC	3.29кв.м	ТЕРАКОТА	ФАЯНС
5	ДНЕВНА С КУХН. БОКС	24.73кв.м	ЛАМПАРКЕТ	ЛАТЕКС
6	БАЛКОН	3.30кв.м	СТУДОУСТ. ГРАНИТОГРЕС	
7	СПАЛНЯ	10.13кв.м	ЛАМПАРКЕТ	ЛАТЕКС
СТЪЛБИЩЕ				
		17.47кв.м	ГРАНИТОГРЕС	ЛАТЕКС

ЗАБЕЛЕЖКИ:
1. РАЗМЕРИТЕ ПО КОТИРОВЪЧНИТЕ ЛИНИИ СА ЗИДАРСКИ, В САНТИМЕТРИ.
2. ОТВОРИТЕ НА ДОГРАМИТЕ СА ЗИДАРСКИ. ДА СЕ ВЗЕМАТ ДОПЪЛНИТЕЛНО МЕРКИ ОТ МЯСТО ЗА ИЗПЪЛНЕНИЕ НА ДОГРАМАТА.
3. ВСИЧКИ ПАРАПЕТИ ДА СЕ ИЗПЪЛНЯТ С ВИСОЧИНА 105 (CM) ОТ ГОТОВ ПОД.
4. ПОДПРОЗОРЕЧНИТЕ ПАРАПЕТИ (ППП) СЕ МЕРЯТ ОТ КОТА ГОТОВ ПОД.
5. ТОПЛОИЗОЛАЦИЯТА ДА СЕ ИЗПЪЛНИ ОТВЪН НА ОГРАДНИТЕ ЕЛЕМЕНТИ.
6. ВИСОЧИНИТЕ НА ВРАТИТЕ СА ОТ КОТА ГОТОВ ПОД
7. ВСИЧКИ ИЗОЛАЦИОННИ РАБОТИ ДА СЕ ИЗПЪЛНЯВАТ ПО ТЕХНИЧЕСКО ПРЕДПИСАНИЕ ОТ ПРОИЗВОДИТЕЛЯ.
8. ВСИЧКИ ЦВЕТОВЕ И МАТЕРИАЛИ, НЕУКАЗАНИ В ЧЕРТЕЖА, СЛЕДВА ДА СЕ ИЗПЪЛНЯТ ПО ДОПЪЛНИТЕЛНО ПРЕДПИСАНИ УКАЗАНИЯ ОТ ПРОЕКТАНТА.
9. ВСИЧКИ КОМИНИ ДА СЕ ИЗЗИДАТ С ОГНЕОПОРНИ ТУХЛИ С КЛАС ПО РЕАКЦИЯ НА ОГЪН А2, С ОГНЕУСТОЙЧИВОСТ G 100. ФУГИТЕ ДА СЕ ЗАПЪЛНЯТ ПО ЦЯЛАТА ВИСОЧИНА.

ОБЩА ПЛОЩ НА НИВОТО-201.86кв.м, в това число 20.63кв.м общи части

ВЪЗПОЖИТЕЛ		СЪГЛАСУВАТЕ:		
"БИЛДИНГ ЕКСПРЕС КР" ЕООД				
ОБЕКТ				
ЖИЛИЩНА СГРАДА И ИЗГРЕБНА ЯМА В УПИ Х-268 (ПИ с идент.68134.1977.2642), КВ.31, м."ДРАГАЛЕВЦИ", РАЙОН "ВИТОША" - СО				
ЧАСТ	АРХИТЕКТУРА	ФАЗА	МАЩАБ	ЛИСТ NO.
		ТП	1:50	3
ОПИСАНИЕ НА ЧЕРТЕЖА				
РАЗПРЕДЕЛЕНИЕ НА КОТА +2.82				
ПЕЧАТ НА ПРОЕКТАНТА		Design:		
				
		СИА ЕСБ ЕООД		
		Тел: +359 87 850 74 04		
		WEB: www.siaesb.bg		
		E-mail: office@siaesb.bg		
ПРОЕКТАНТИ		ПРОЕКТАНТИ		ПОДПИС
1.ПРОЕКТАНТ	2.СЪГЛАСУВАЩ	1.ПРОЕКТАНТ	2.СЪГЛАСУВАЩ	
АРХИТЕКТУРА		ОВК/ЕЕ		
арх.Елена Ценова		инж.Григор Зарков		
КОНСТРУКЦИИ		пб		
инж.Антон Милчев		инж.Слава Милчева		
ЕЛЕКТРО ИНСТАЛАЦИИ		ГЕОДЕЗИЯ И ВП		
инж.Светлин Стайков		инж.Александър Милчев		
Вик		ПАРКОУСТРОЙСТВО		
инж.Даниел Господинов		л.арх.Вероника Алексиева		
ПРОЕКТ N	РЕВИЗИЯ	ГОДИНА НА ИЗДАВАНЕ		
	00	2018		