


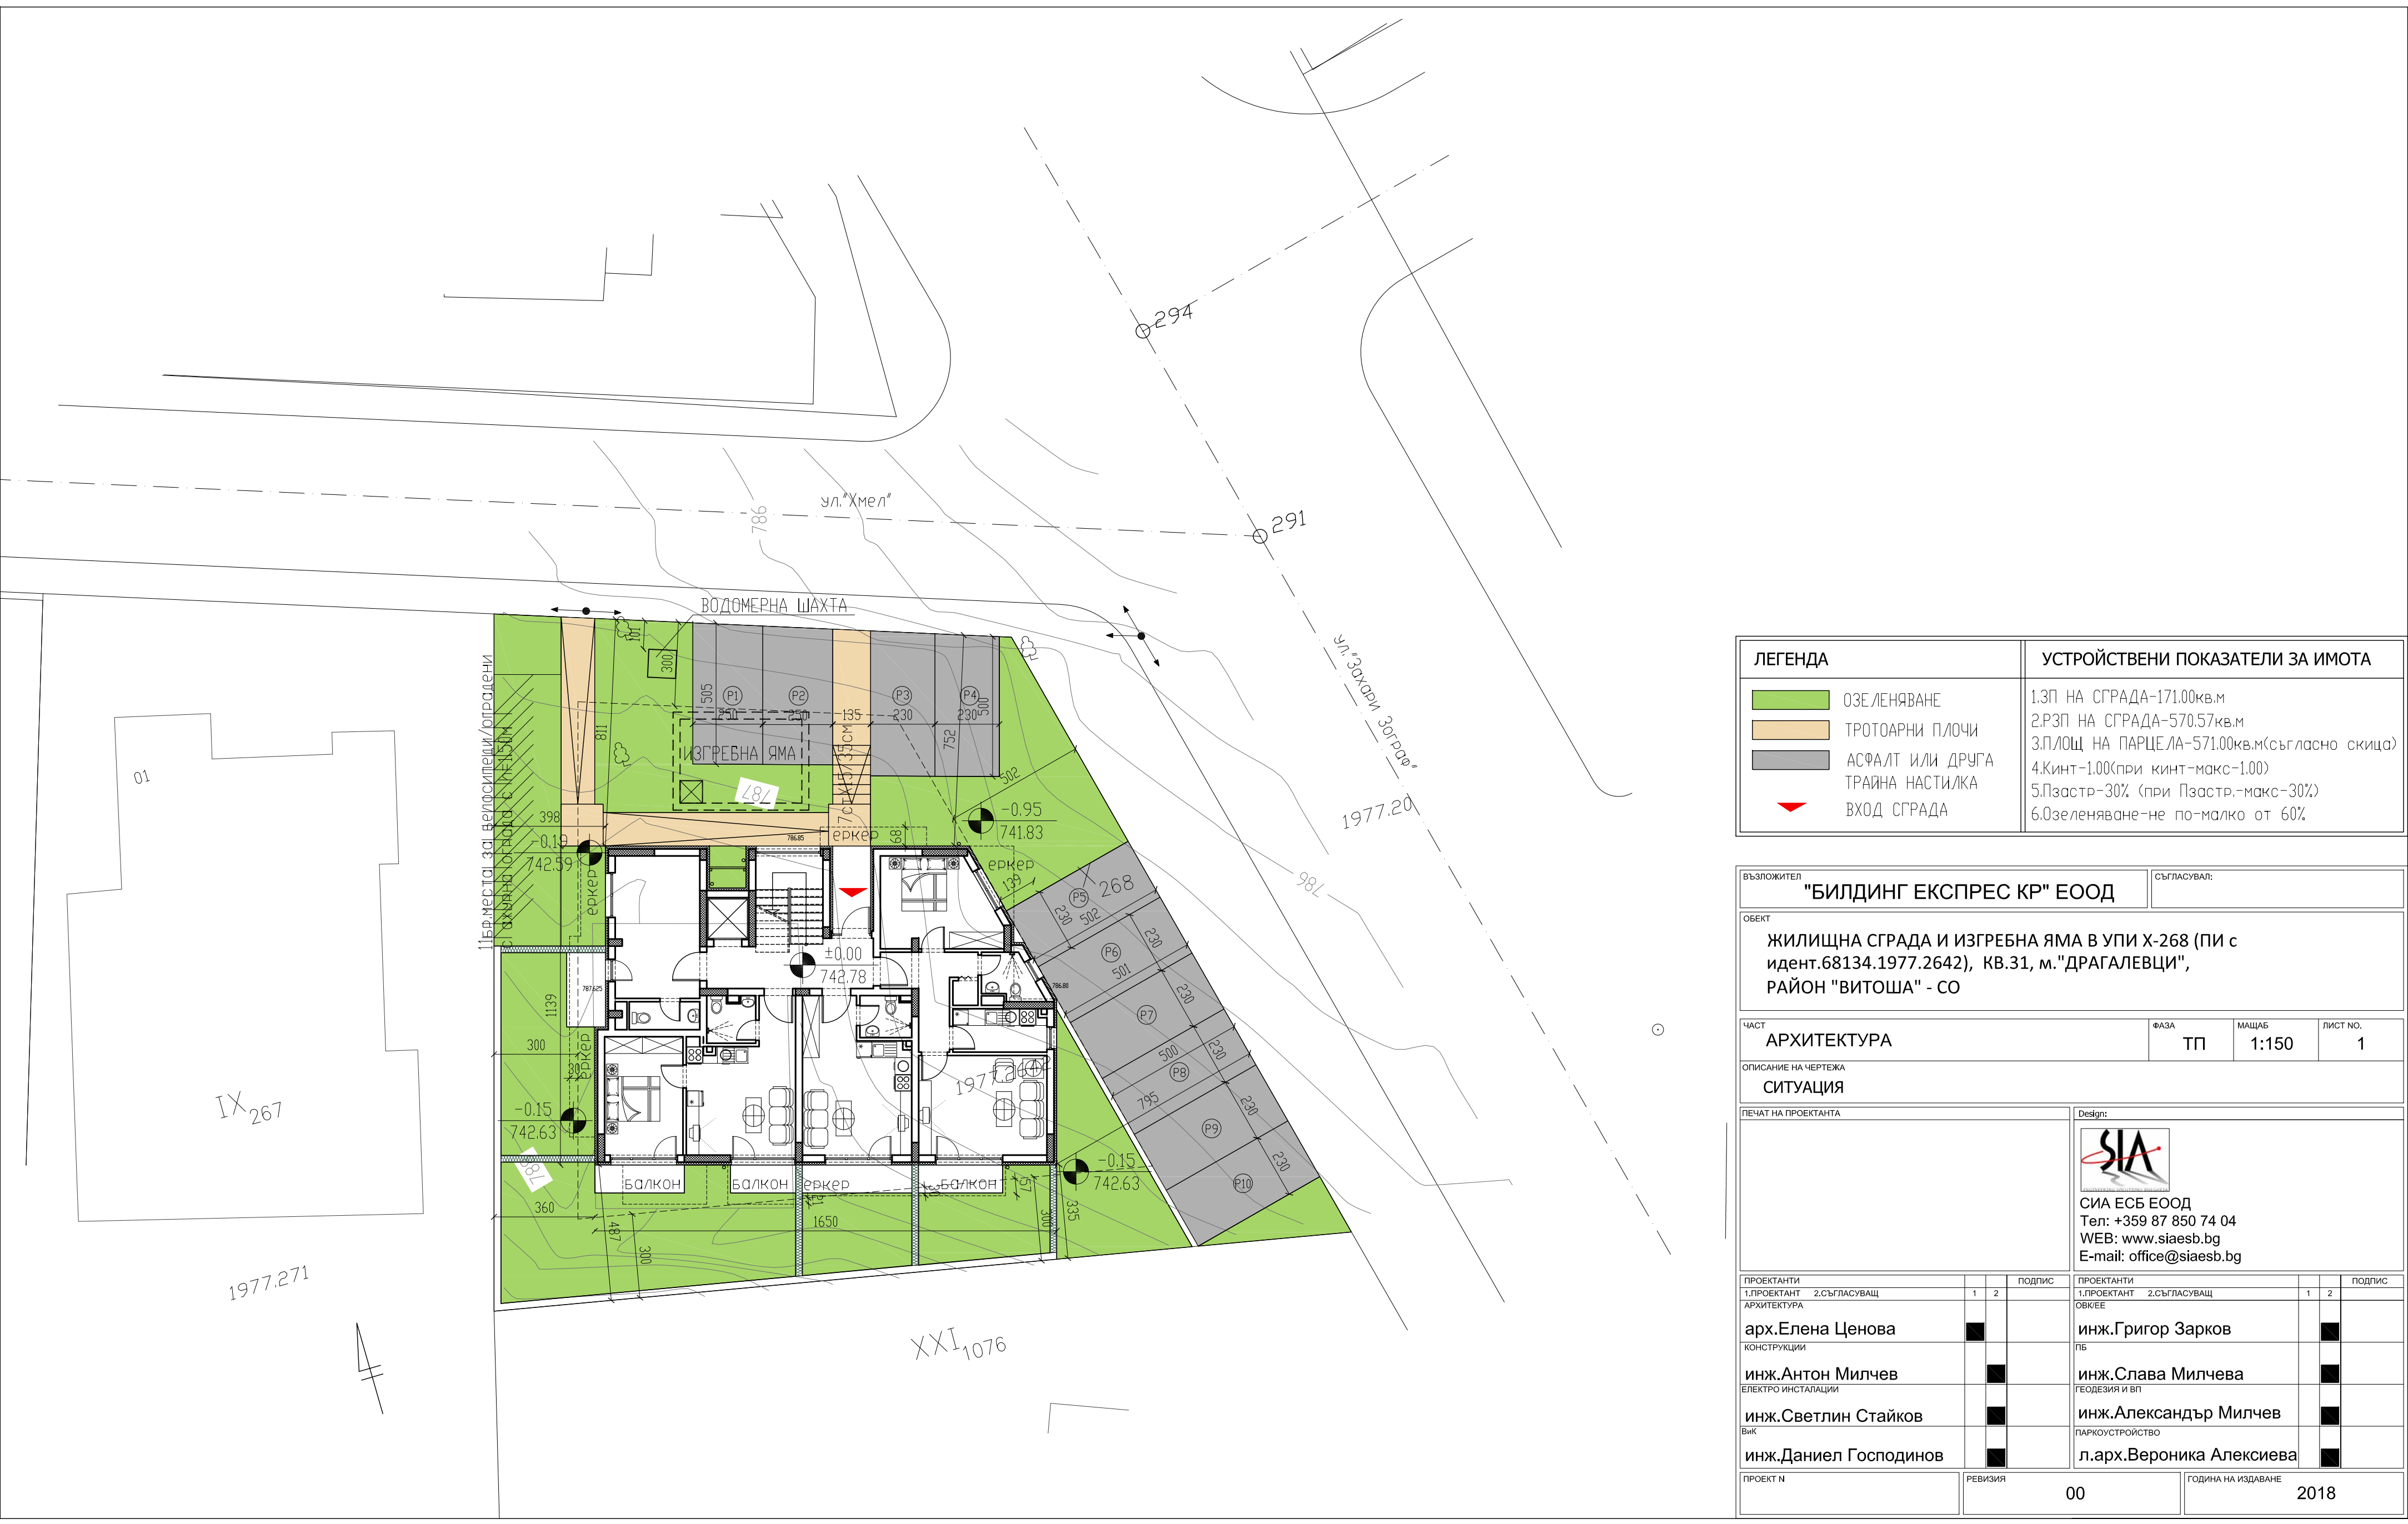

ЛЕГЕНДА	УСТРОЙСТВЕНИ ПОКАЗАТЕЛИ ЗА ИМОТА
ОЗЕЛЕНЯВАНЕ	1.ЗП НА СГРАДА-171.00кв.м
ТРОТОАРНИ ПЛОЧИ	2.РЗП НА СГРАДА-570.57кв.м
АСФАЛТ ИЛИ ДРУГА ТРАЙНА НАСТИЛКА	3.ПЛОЩ НА ПАРЦЕЛА-571.00кв.м(съгласно скица)
ВХОД СГРАДА	4.Кинт-1.00(при кинт-макс-1.00)
	5.Пзастр-30% (при Пзастр.-макс-30%)
	6.Озеленяване-не по-малко от 60%

Възложител "БИЛДИНГ ЕКСПРЕС КР" ЕООД		Съгласувал:		
Обект Жилищна сграда и изгребна яма в УПИ Х-268 (ПИ с идент.68134.1977.2642), кв.31, м."ДРАГАЛЕВЦИ", район "ВИТОША" - СО				
Часть АРХИТЕКТУРА		Фаза ТП	Масштаб 1:150	Лист No. 1
Описание на чертежа СИТУАЦИЯ				
Печат на проектанта		Design:		
		 СИА ЕСБ ЕООД Тел: +359 87 850 74 04 WEB: www.siaesb.bg E-mail: office@siaesb.bg		
Проектанти 1.ПРОЕКТАНТ АРХИТЕКТУРА арх.Елена Ценова КОНСТРУКЦИИ инж.Антон Милчев ЕЛЕКТРО ИНСТАЛАЦИИ инж.Светлин Стайков Вик инж.Даниел Господинов		Проектанти 1.ПРОЕКТАНТ 2.СЪГЛАСУВАЩ ОВК/ЕЕ инж.Григор Зарков ПБ инж.Слава Милчева ГЕОДЕЗИЯ И ВП инж.Александър Милчев ПАРКОУСТРОЙСТВО л.арх.Вероника Алексиева		
Проект N		Ревизия 00		Година на издаване 2018